Fine moulded frames

Hallway / W1 - Rear external door

All dimensions in mm. Frame sizes include the moulding. Blue chains include gaps and openings.

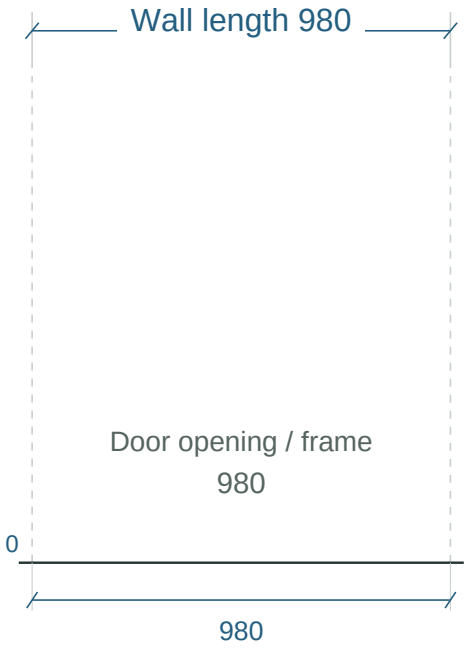

0 = Rear-recess side. Measure along this wall from the 0 point shown.

No dado or frames on this wall.

Mark each frame edge from the same 0 point. Far-end distances start at the frame right edge.
Heights are from the local floor. Lower wall zone only; drawing scales vary. Do not scale from the page.
Rounded layout; dimensions match the fine moulded frames model. Check the wall length on site.

Fine moulded frames

Hallway / W2 - Bathroom wall

All dimensions in mm. Frame sizes include the moulding. Blue chains include gaps and openings.

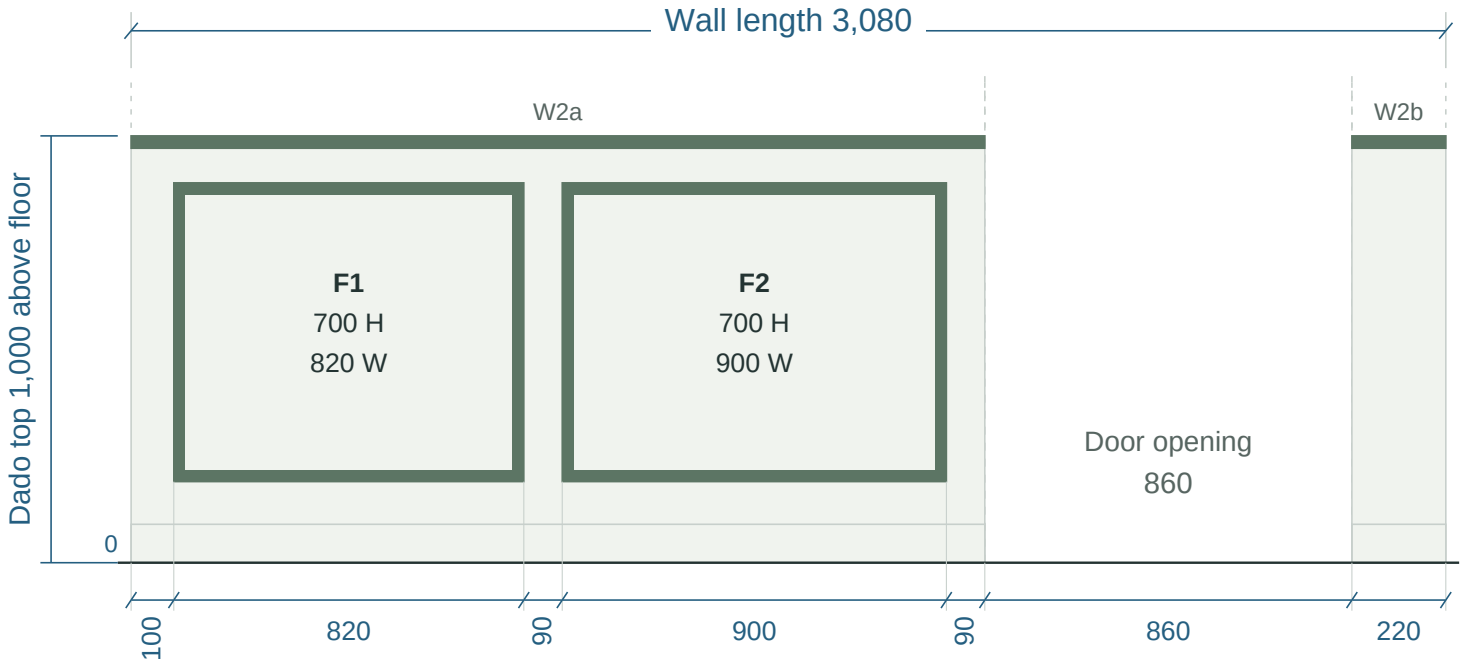

0 = Rear-door plane / rear-wall corner. Measure along this wall from the 0 point shown.

Frame	Height	Width	Left edge from 0	Right edge from 0	To far wall end	Gap to next frame
F1	700	820	100	920	2,160	90
F2	700	900	1,010	1,910	1,170	-

Frame bottom 190 / top 890 above the local floor. Mark the outside moulding edges.

Dado lengths: W2a 2,000 | W2b 220 | Section: 29 high x 15 deep

Mark each frame edge from the same 0 point. Far-end distances start at the frame right edge.
Heights are from the local floor. Lower wall zone only; drawing scales vary. Do not scale from the page.
Rounded layout; dimensions match the fine moulded frames model. Check the wall length on site.

Source: fine-frame option 02-picture-frames, revision 25 October 2026. Frames continue behind radiators.

Fine moulded frames

Hallway / W3 - Wedding-photo wall

All dimensions in mm. Frame sizes include the moulding. Blue chains include gaps and openings.

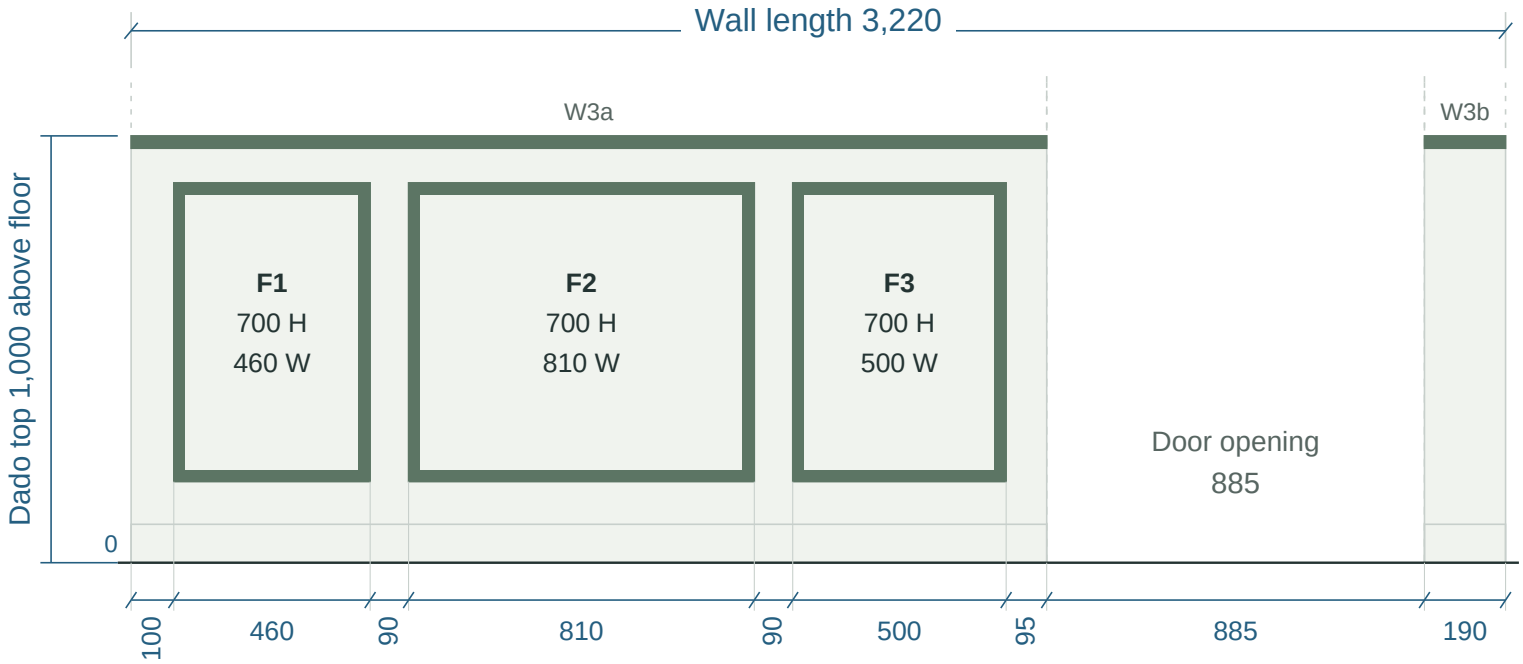

0 = Bathroom-wall corner. Measure along this wall from the 0 point shown.

Frame	Height	Width	Left edge from 0	Right edge from 0	To far wall end	Gap to next frame
F1	700	460	100	560	2,660	90
F2	700	810	650	1,460	1,760	90
F3	700	500	1,550	2,050	1,170	-

Frame bottom 190 / top 890 above the local floor. Mark the outside moulding edges.

Dado lengths: W3a 2,145 | W3b 190 | Section: 29 high x 15 deep

Mark each frame edge from the same 0 point. Far-end distances start at the frame right edge.
Heights are from the local floor. Lower wall zone only; drawing scales vary. Do not scale from the page.
Rounded layout; dimensions match the fine moulded frames model. Check the wall length on site.

Source: fine-frame option 02-picture-frames, revision 25 October 2026. Frames continue behind radiators.

Fine moulded frames

Hallway / W4 - Storage wall

All dimensions in mm. Frame sizes include the moulding. Blue chains include gaps and openings.

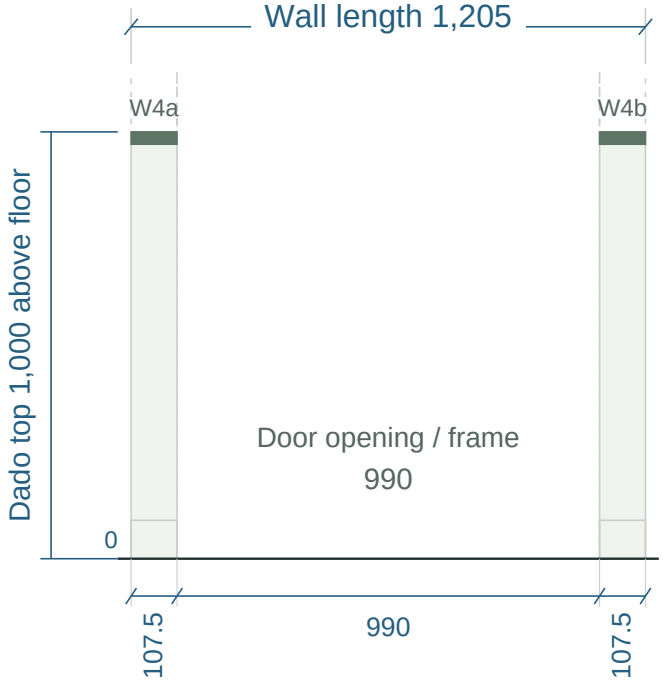

0 = Wedding-photo-wall corner. Measure along this wall from the 0 point shown.

Dado only - no frames on this wall.

Dado lengths: W4a 107.5 | W4b 107.5 | Section: 29 high x 15 deep

Mark each frame edge from the same 0 point. Far-end distances start at the frame right edge.
Heights are from the local floor. Lower wall zone only; drawing scales vary. Do not scale from the page.
Rounded layout; dimensions match the fine moulded frames model. Check the wall length on site.

Source: fine-frame option 02-picture-frames, revision 25 October 2026. Frames continue behind radiators.

Fine moulded frames

Hallway / W5 - Entrance and spare-bedroom wall

All dimensions in mm. Frame sizes include the moulding. Blue chains include gaps and openings.

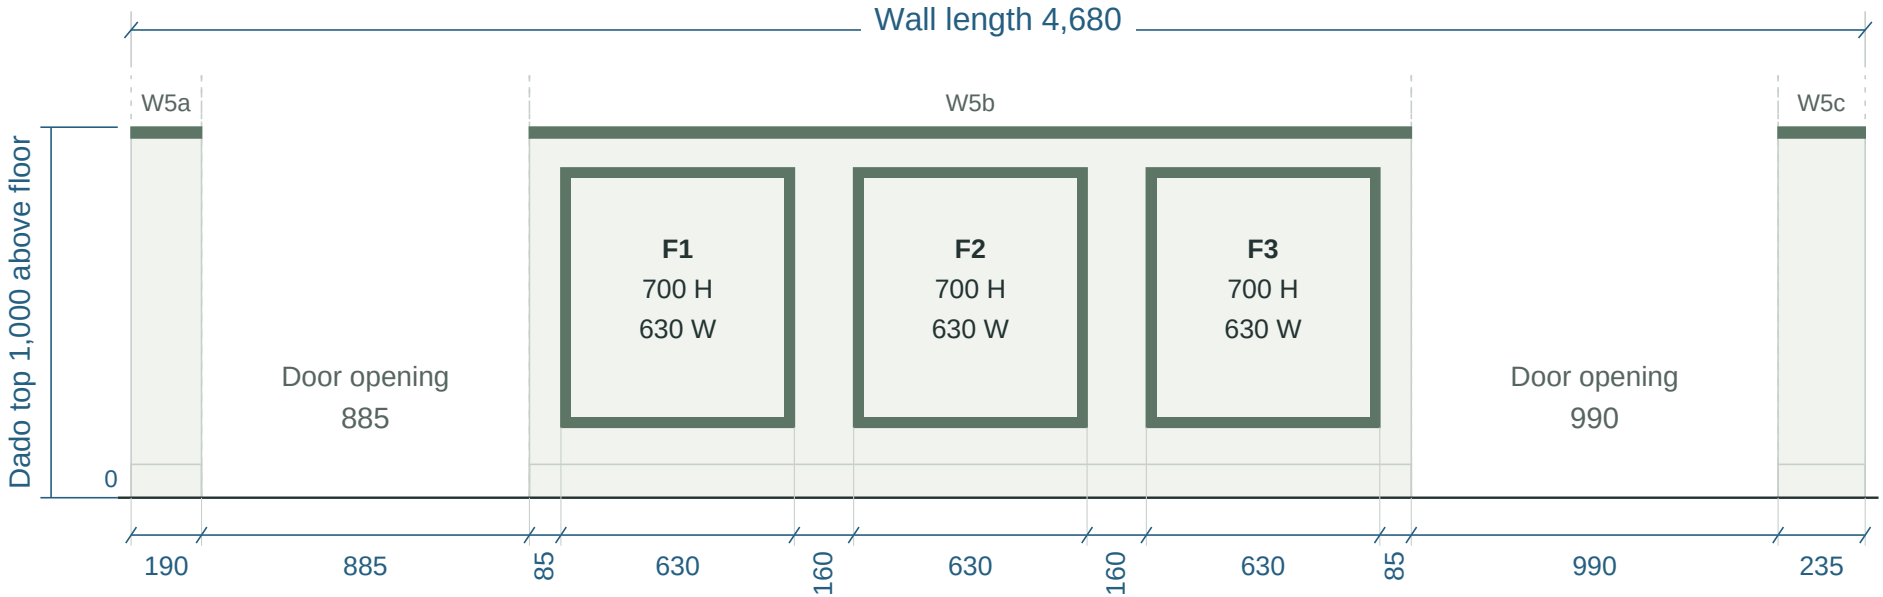

0 = Storage-wall corner. Measure along this wall from the 0 point shown.

Frame	Height	Width	Left edge from 0	Right edge from 0	To far wall end	Gap to next frame
F1	700	630	1,160	1,790	2,890	160
F2	700	630	1,950	2,580	2,100	160
F3	700	630	2,740	3,370	1,310	-

Frame bottom 190 / top 890 above the local floor. Mark the outside moulding edges.

Dado lengths: W5a 190 | W5b 2,380 | W5c 235 | Section: 29 high x 15 deep

Mark each frame edge from the same 0 point. Far-end distances start at the frame right edge.
Heights are from the local floor. Lower wall zone only; drawing scales vary. Do not scale from the page.
Rounded layout; dimensions match the fine moulded frames model. Check the wall length on site.

Source: fine-frame option 02-picture-frames, revision 25 October 2026. Frames continue behind radiators.

Fine moulded frames

Hallway / W6 - Kitchen and cabinet wall

All dimensions in mm. Frame sizes include the moulding. Blue chains include gaps and openings.

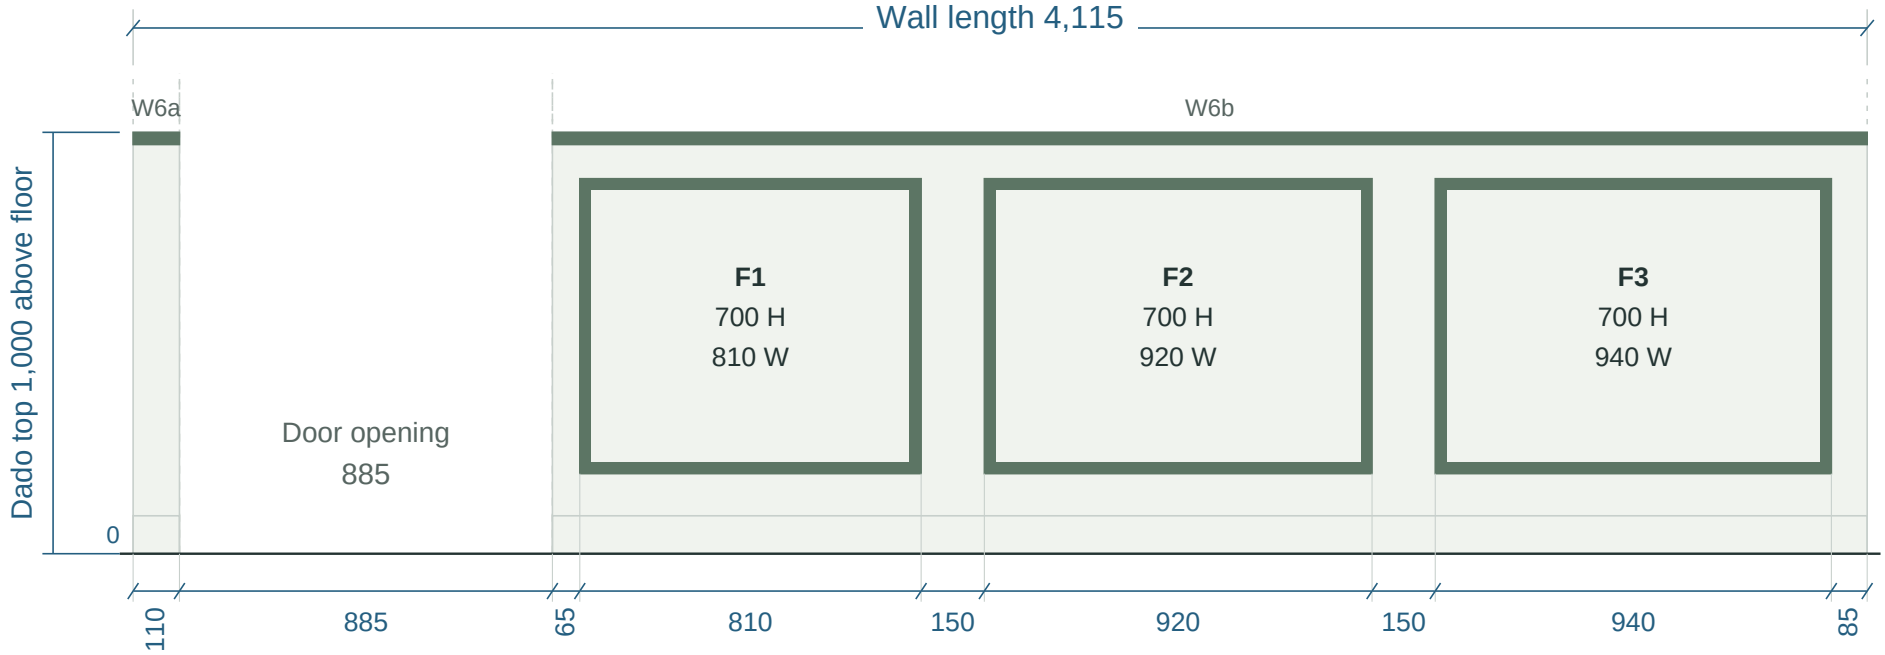

0 = Entrance/spare-bedroom-wall corner. Measure along this wall from the 0 point shown.

Frame	Height	Width	Left edge from 0	Right edge from 0	To far wall end	Gap to next frame
F1	700	810	1,060	1,870	2,245	150
F2	700	920	2,020	2,940	1,175	150
F3	700	940	3,090	4,030	85	-

Frame bottom 190 / top 890 above the local floor. Mark the outside moulding edges.

Dado lengths: W6a 110 | W6b 3,120 | Section: 29 high x 15 deep

Mark each frame edge from the same 0 point. Far-end distances start at the frame right edge.
Heights are from the local floor. Lower wall zone only; drawing scales vary. Do not scale from the page.
Rounded layout; dimensions match the fine moulded frames model. Check the wall length on site.

Source: fine-frame option 02-picture-frames, revision 25 October 2026. Frames continue behind radiators.

Fine moulded frames

Hallway / W7 - Rear boxing face

All dimensions in mm. Frame sizes include the moulding. Blue chains include gaps and openings.

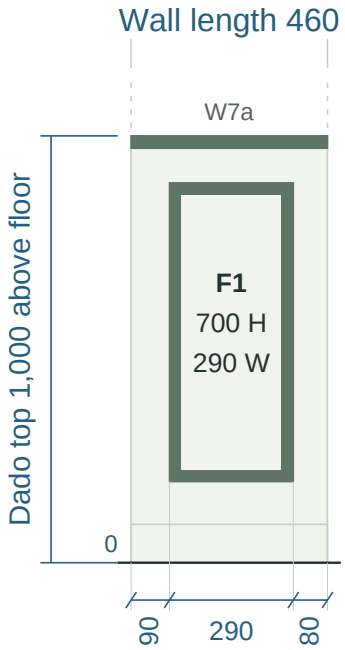

0 = Kitchen-wall corner. Measure along this wall from the 0 point shown.

Frame	Height	Width	Left edge from 0	Right edge from 0	To far wall end	Gap to next frame
F1	700	290	90	380	80	-

Frame bottom 190 / top 890 above the local floor. Mark the outside moulding edges.

Dado lengths: W7a 460 | Section: 29 high x 15 deep

Mark each frame edge from the same 0 point. Far-end distances start at the frame right edge.
Heights are from the local floor. Lower wall zone only; drawing scales vary. Do not scale from the page.
Rounded layout; dimensions match the fine moulded frames model. Check the wall length on site.

Source: fine-frame option 02-picture-frames, revision 25 October 2026. Frames continue behind radiators.

Fine moulded frames

Hallway / W8 - Rear recess return

All dimensions in mm. Frame sizes include the moulding. Blue chains include gaps and openings.

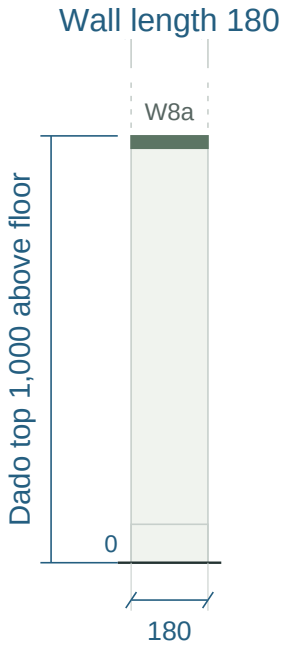

0 = Boxing-face corner. Measure along this wall from the 0 point shown.

Dado only - no frames on this wall.

Dado lengths: W8a 180 | Section: 29 high x 15 deep

Mark each frame edge from the same 0 point. Far-end distances start at the frame right edge.
Heights are from the local floor. Lower wall zone only; drawing scales vary. Do not scale from the page.
Rounded layout; dimensions match the fine moulded frames model. Check the wall length on site.

Source: fine-frame option 02-picture-frames, revision 25 October 2026. Frames continue behind radiators.

Fine moulded frames

Entrance / E1 - Barn-door wall

All dimensions in mm. Frame sizes include the moulding. Blue chains include gaps and openings.

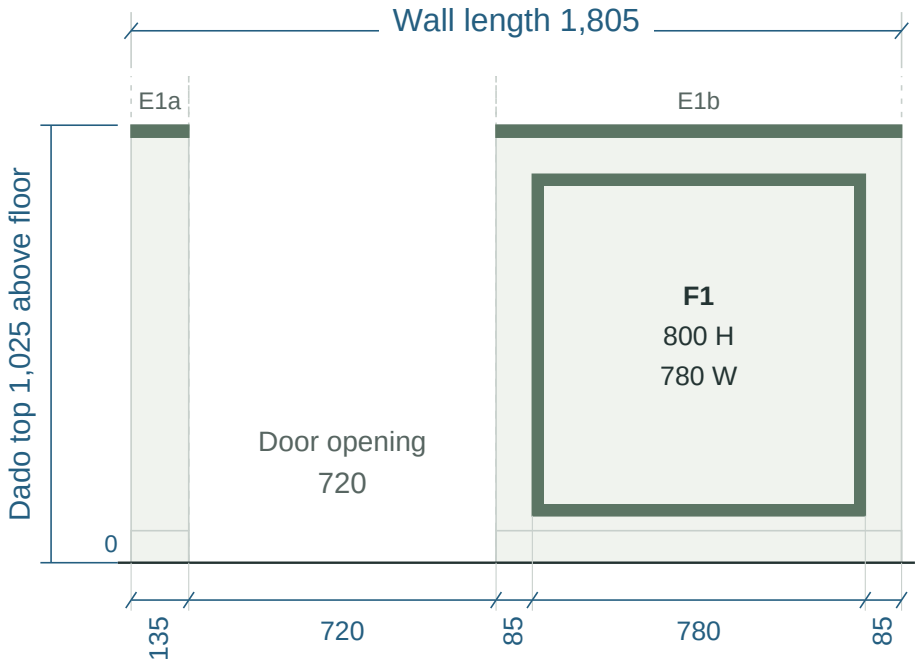

0 = Connecting-wall corner. Measure along this wall from the 0 point shown.

Frame	Height	Width	Left edge from 0	Right edge from 0	To far wall end	Gap to next frame
F1	800	780	940	1,720	85	-

Frame bottom 110 / top 910 above the local floor. Mark the outside moulding edges.

Dado lengths: E1a 135 | E1b 950 | Section: 28 high x 9 deep

Mark each frame edge from the same 0 point. Far-end distances start at the frame right edge.
Heights are from the local floor. Lower wall zone only; drawing scales vary. Do not scale from the page.
Rounded layout; dimensions match the fine moulded frames model. Check the wall length on site.

Source: fine-frame option 02-picture-frames, revision 25 October 2026. Frames continue behind radiators.

Fine moulded frames

Entrance / E2 - Front-door wall

All dimensions in mm. Frame sizes include the moulding. Blue chains include gaps and openings.

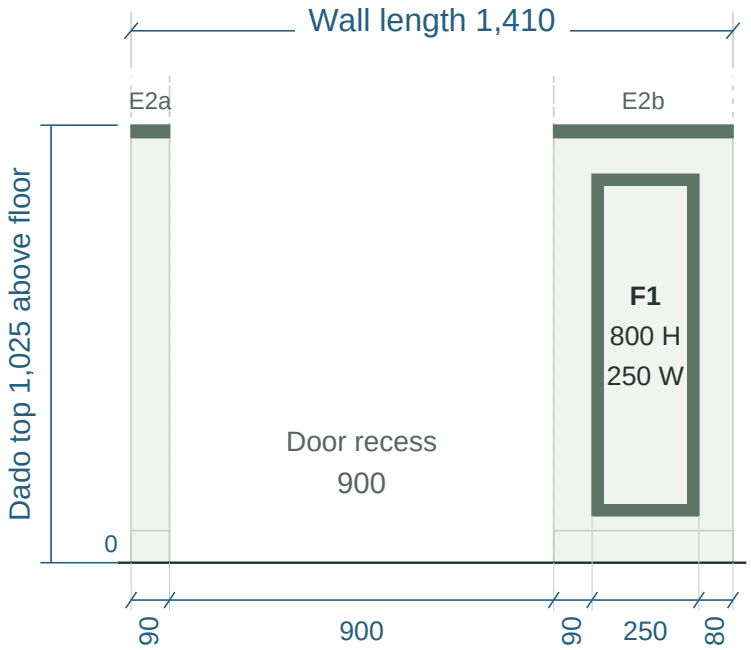

0 = Barn-door-wall corner. Measure along this wall from the 0 point shown.

Frame	Height	Width	Left edge from 0	Right edge from 0	To far wall end	Gap to next frame
F1	800	250	1,080	1,330	80	-

Frame bottom 110 / top 910 above the local floor. Mark the outside moulding edges.

Dado lengths: E2a 90 | E2b 420 | Section: 29 high x 15 deep

Mark each frame edge from the same 0 point. Far-end distances start at the frame right edge.
Heights are from the local floor. Lower wall zone only; drawing scales vary. Do not scale from the page.
Rounded layout; dimensions match the fine moulded frames model. Check the wall length on site.

Source: fine-frame option 02-picture-frames, revision 25 October 2026. Frames continue behind radiators.

Fine moulded frames

Entrance / E3 - Mirror and radiator wall

All dimensions in mm. Frame sizes include the moulding. Blue chains include gaps and openings.

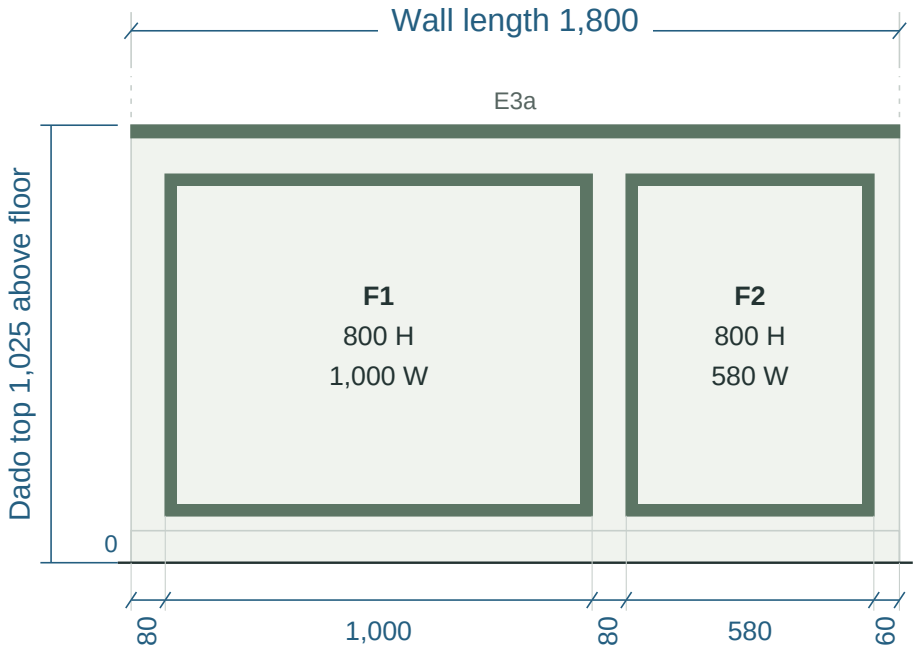

0 = Front-door-wall corner. Measure along this wall from the 0 point shown.

Frame	Height	Width	Left edge from 0	Right edge from 0	To far wall end	Gap to next frame
F1	800	1,000	80	1,080	720	80
F2	800	580	1,160	1,740	60	-

Frame bottom 110 / top 910 above the local floor. Mark the outside moulding edges.

Dado lengths: E3a 1,800 | Section: 29 high x 15 deep

Mark each frame edge from the same 0 point. Far-end distances start at the frame right edge.
Heights are from the local floor. Lower wall zone only; drawing scales vary. Do not scale from the page.
Rounded layout; dimensions match the fine moulded frames model. Check the wall length on site.

Source: fine-frame option 02-picture-frames, revision 25 October 2026. Frames continue behind radiators.

Fine moulded frames

Entrance / E4 - Connecting wall

All dimensions in mm. Frame sizes include the moulding. Blue chains include gaps and openings.

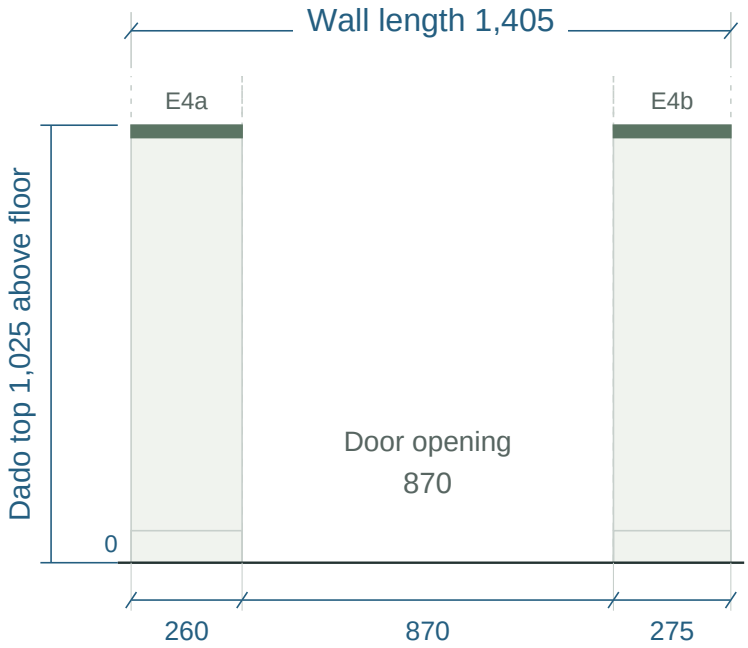

0 = Mirror-wall corner. Measure along this wall from the 0 point shown.

Dado only - no frames on this wall.

Dado lengths: E4a 260 | E4b 275 | Section: 29 high x 15 deep

Mark each frame edge from the same 0 point. Far-end distances start at the frame right edge.
Heights are from the local floor. Lower wall zone only; drawing scales vary. Do not scale from the page.
Rounded layout; dimensions match the fine moulded frames model. Check the wall length on site.

Source: fine-frame option 02-picture-frames, revision 25 October 2026. Frames continue behind radiators.